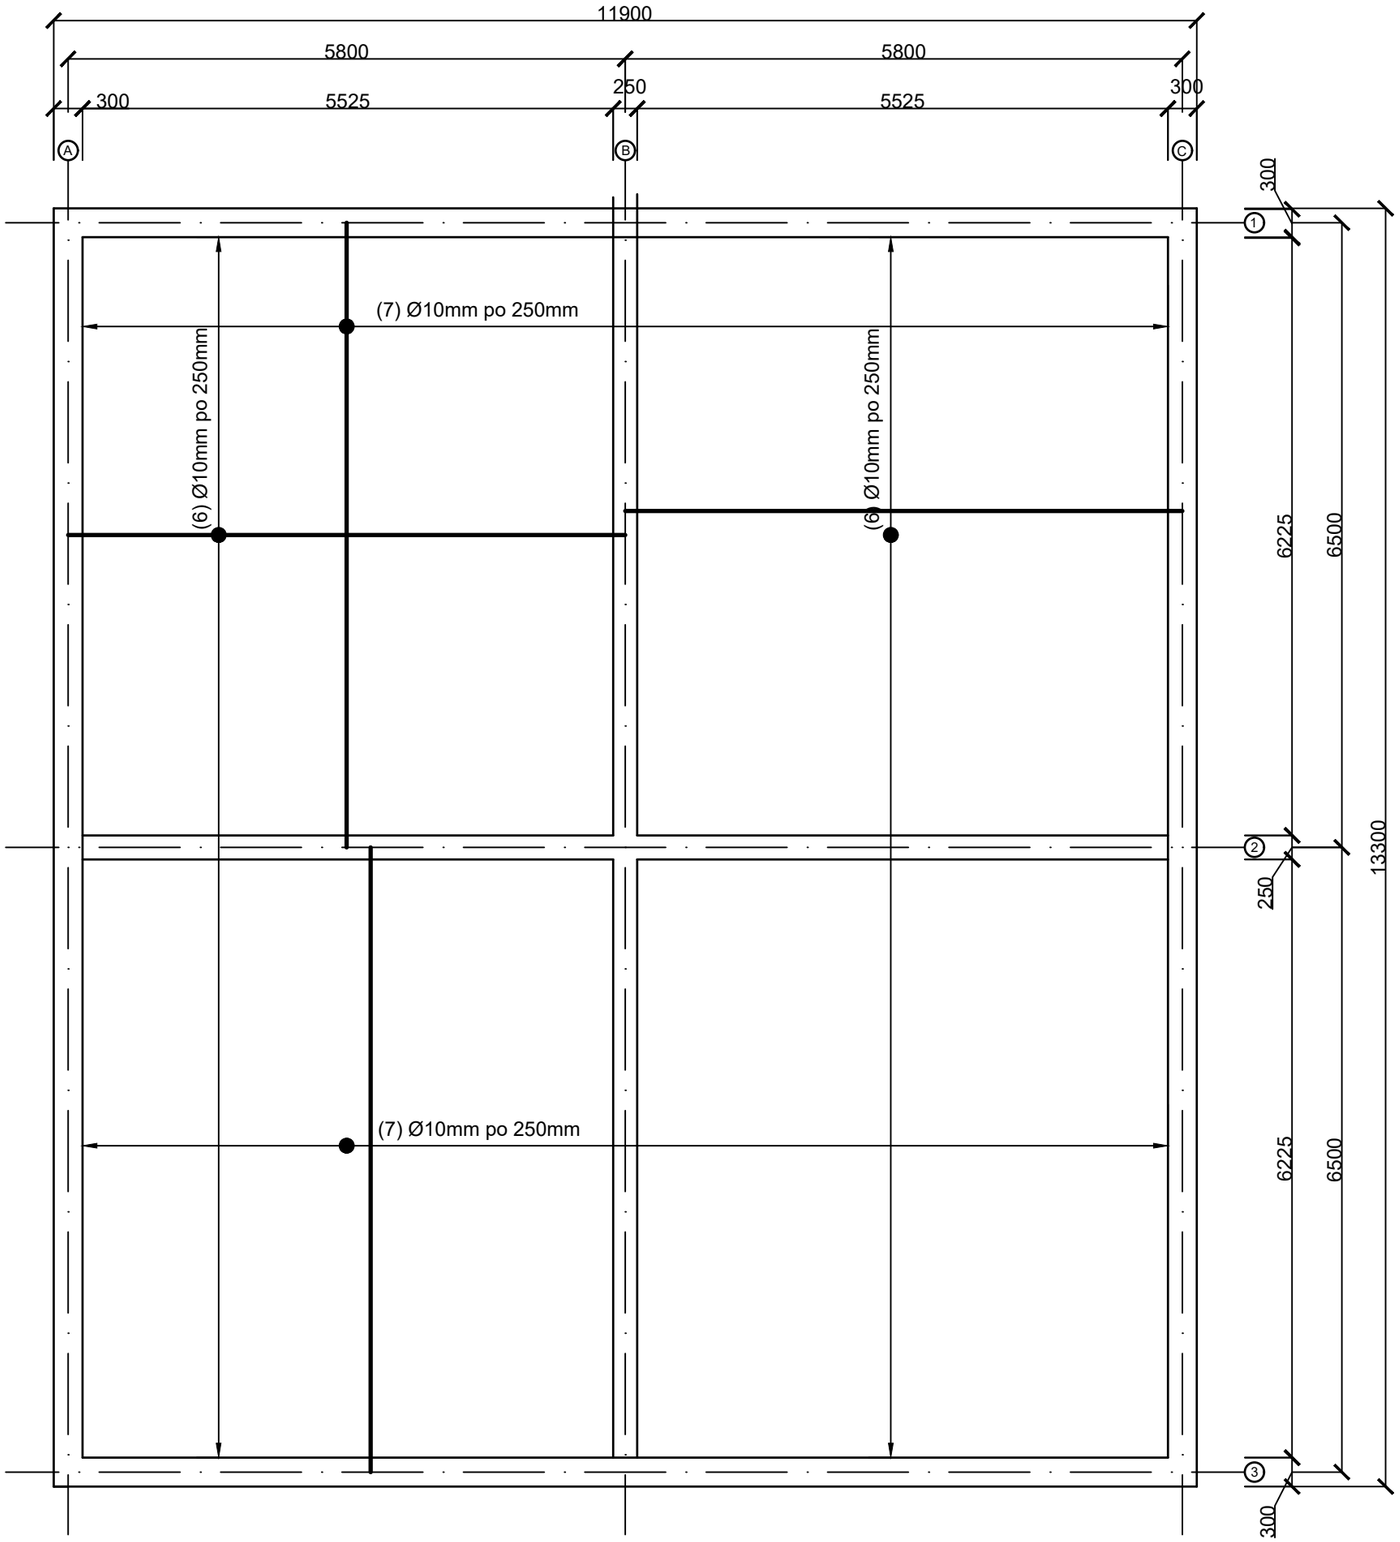

POLOŽKY VÝZTUŽE

(2) Ø10mm, L = 5750 mm, 150 ks

(2) Ø10mm, L = 6450 mm, 150 ks

Č.P	Ø [mm]	Délka [mm]	ks	Celková délka [m]
1	10	5750	92	529,0
2	10	6450	102	657,9
Celková délka dle Ø [m]				1186,9000
Hmotnost Ø na 1bm [kg/m´]				0,617
Hmotnost celkem [kg]				732,3173

Vlasnosti materiálu

OCEL: B500B
BETON: C25/30 - XC1 - CL0,2 - Dmax 22mm - S3
Krycí vrstva výztuže: c = 30mm

VÝZTUŽ KÓTOVÁNA NA OSU

Zpracoval: Borecký Petr	Vedoucí cvičení: Ing. Jiří Kovář	Školní rok: 2025/26	Fakulta stavební ČVUT
Předmět: RBZS			
Název úlohy: Výkres výztuže desky		Datum:	2.11.25
		Měřítko:	1:60
		Číslo výkresu:	2
Název výkresu: Dolní výztuž			