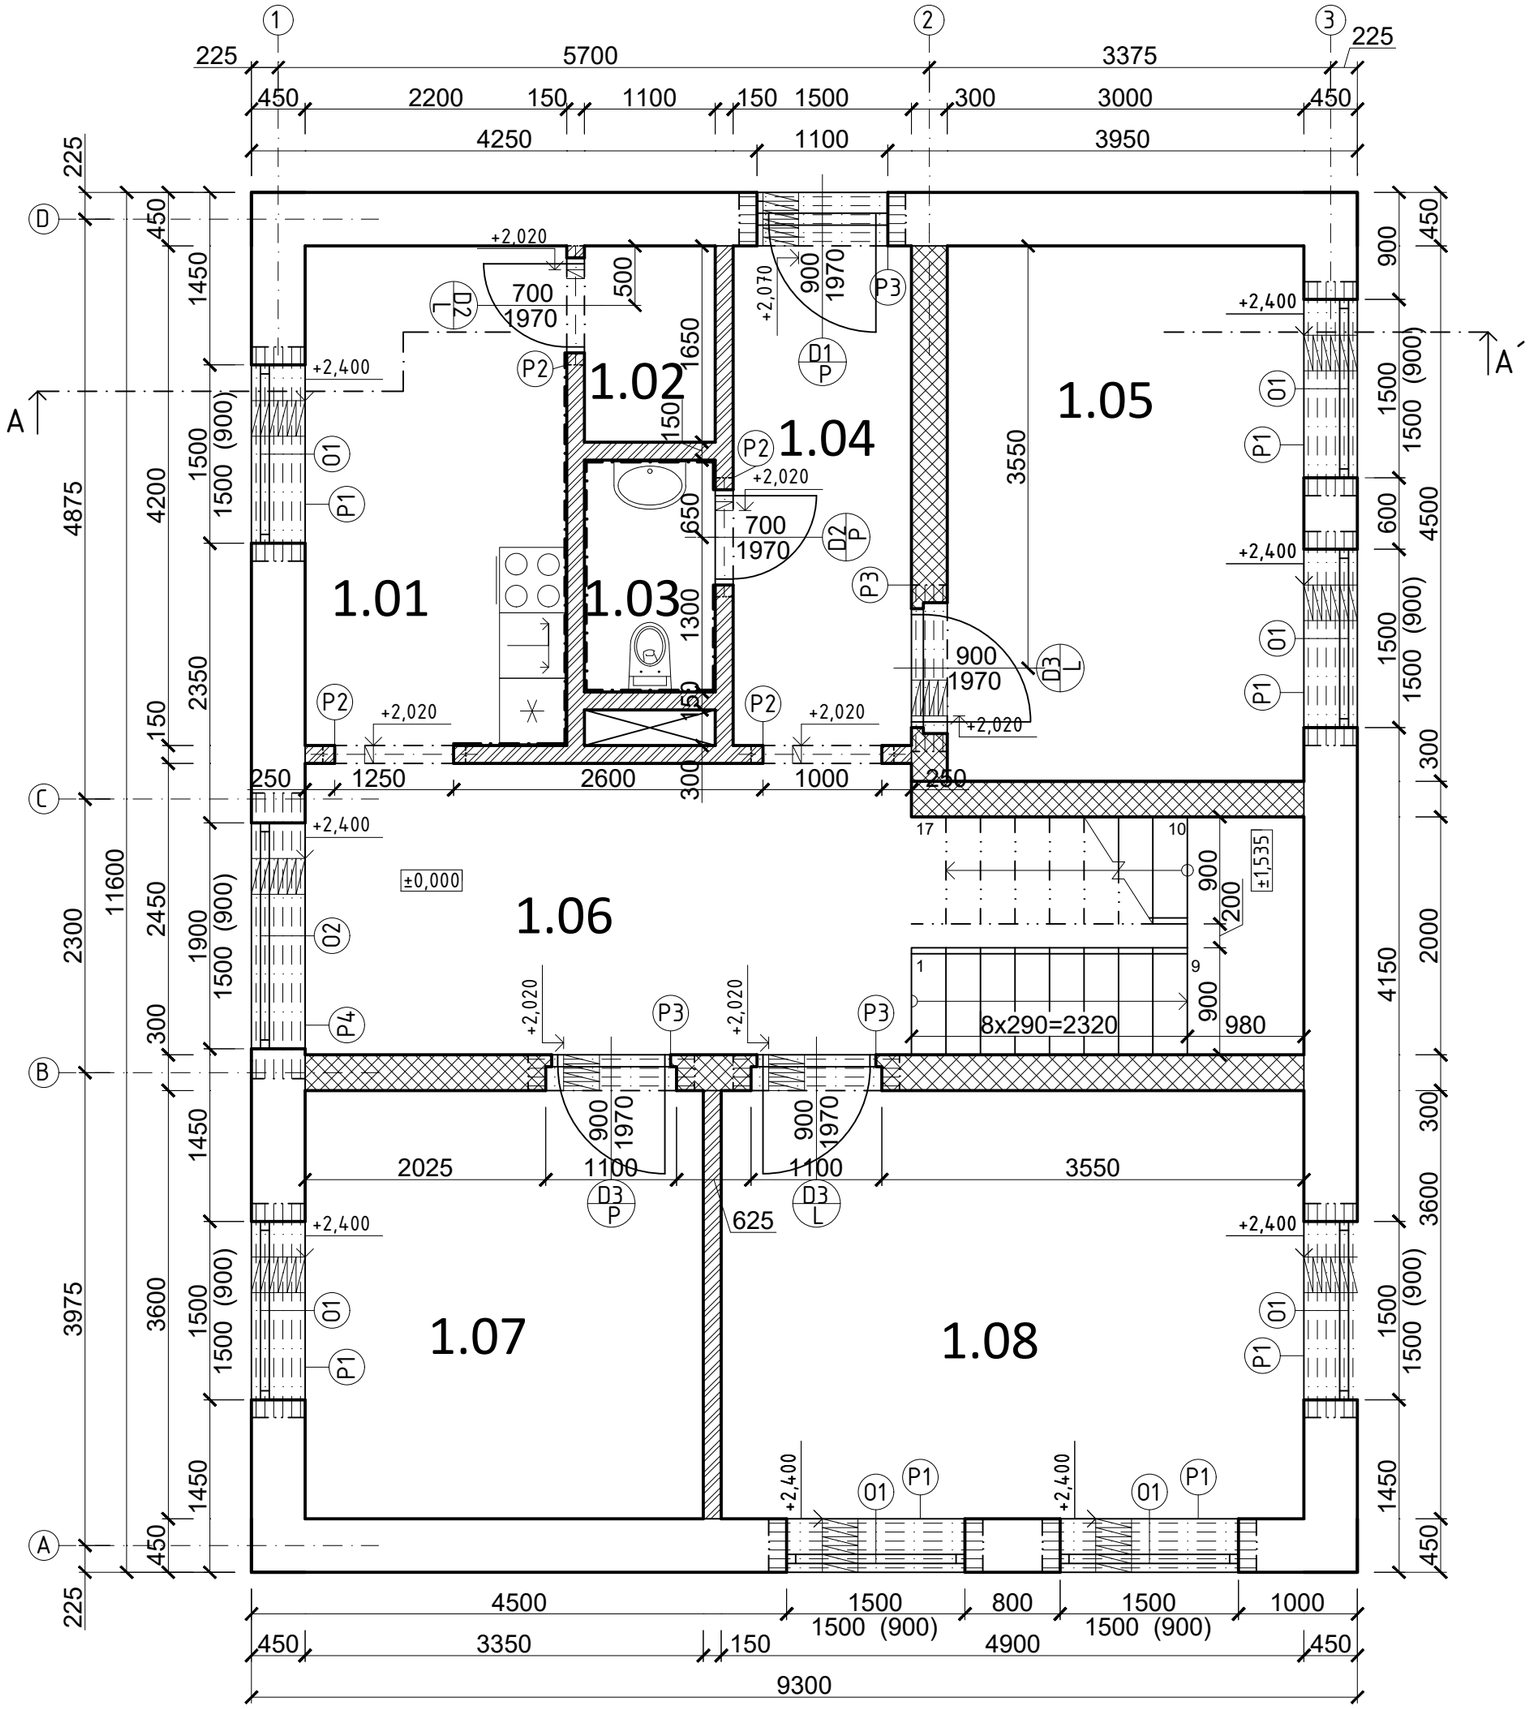

LEGENDA MÍSTNOSTÍ

Č. M.	Účel místnosti	Plocha [m²]	Úprava místnosti	Úprava stěn
1.01	Kuchyň	9,24	Keramická dlažba	Sádrová omítka
1.02	Spižírna	1,82	Keramická dlažba	Vápená omítka
1.03	WC	2,2	Keramická dlažba	Sádrová omítka
1.04	Chodba	6,1	Laminátová podlaha	Vápená omítka
1.05	Pracovna	13,5	Koberec	Vápená omítka
1.06	Jídelna	13,1	Laminátová podlaha	Vápená omítka
1.07	Pokoj pro hosty	12,1	Koberec	Vápená omítka
1.08	Obývací pokoj	17,6	Koberec	Účel místnosti

LEGENDA MATERIÁLŮ

- Obvodové nosné zdivo
- Vnitřní nosné zdivo
- Vnitřní nosné zdivo
- Železobeton
- Zemina

S

STUDENT	Petr Borecký		
VYUČUJÍCÍ	Ing. Jakub Mazura		
PŘEDMĚT	124 PSI1	FORMÁT	A3
		MĚŘÍTKO	1:50
		DATUM	10/2024
OBSAH :	VYKRESLENÍ	Č. VÝKR. 1	ČV