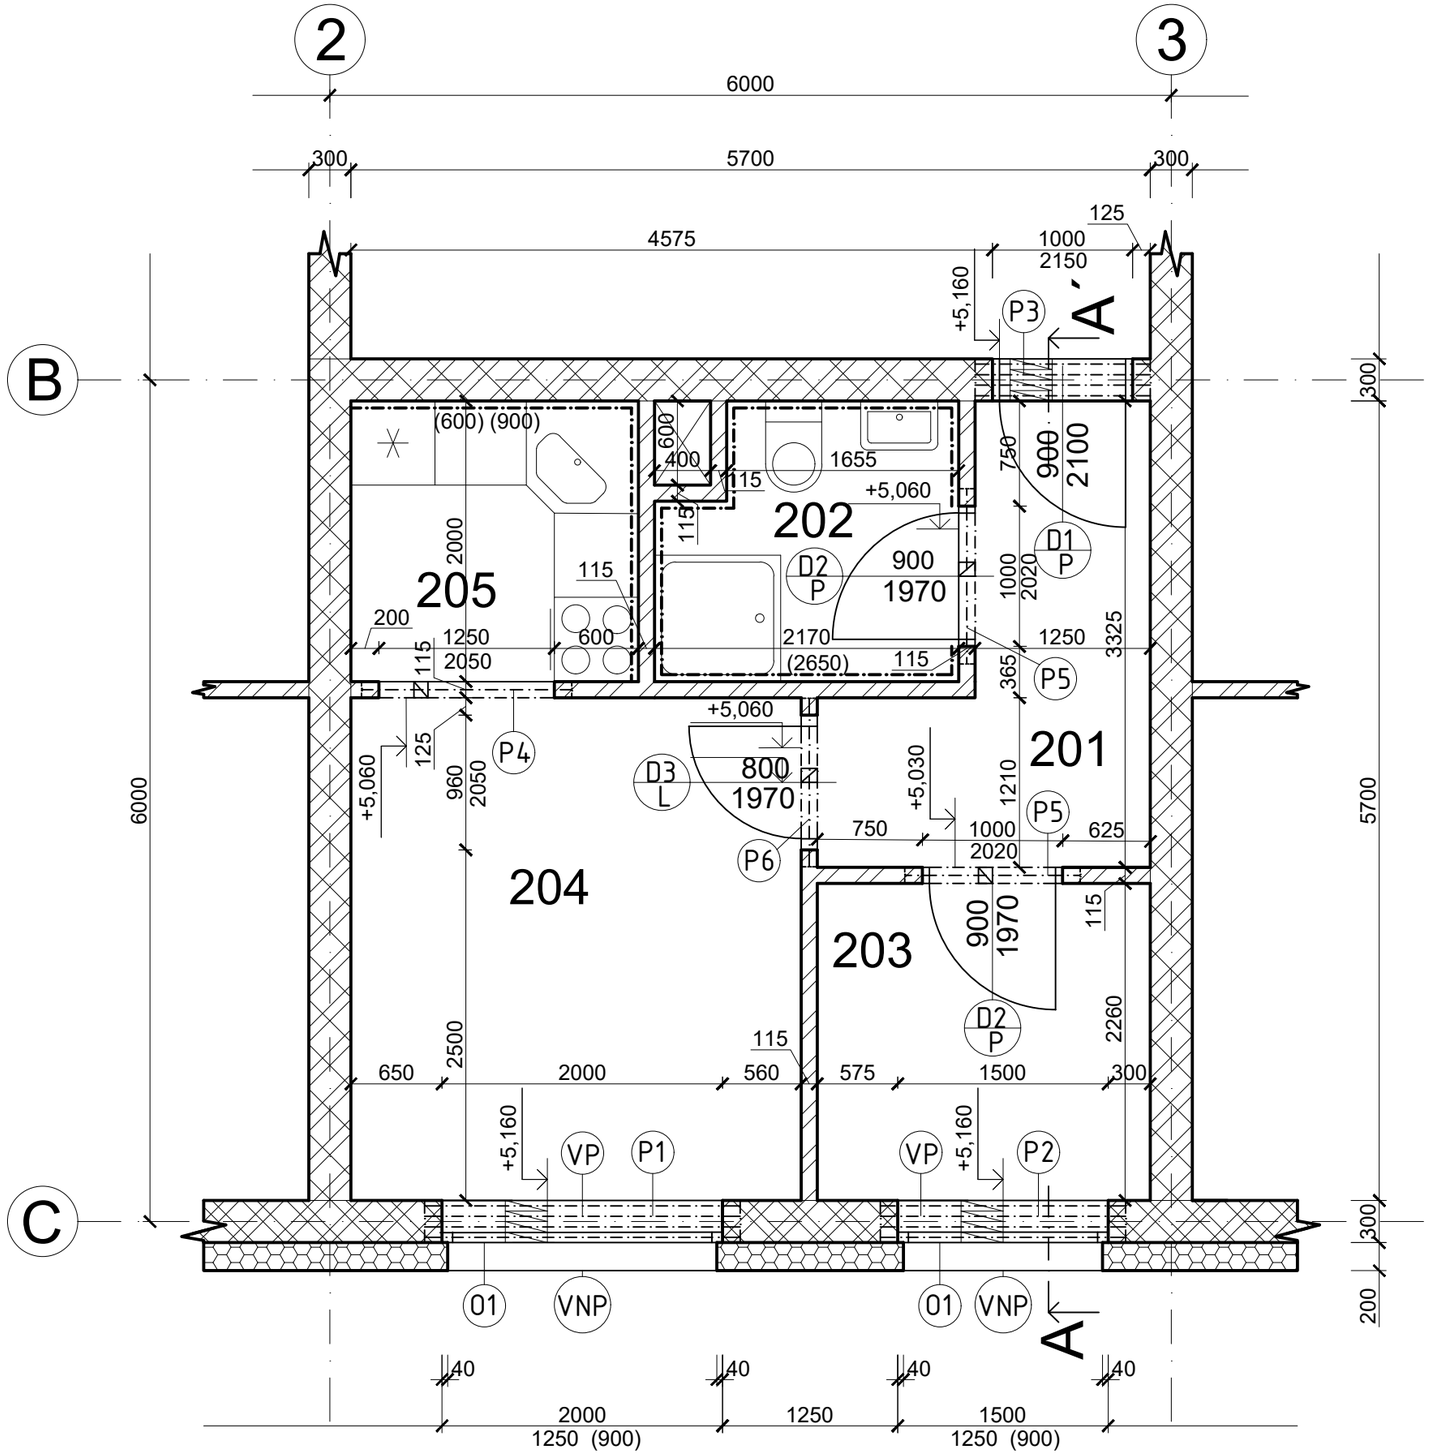

LEGENDA MÍSTNOSTÍ

Č. M.	Účel místnosti	Plocha [m²]	Úprava místnosti
201	Chodba	5,52	Vinyl
202	Koupelna	3,97	Keramická dlažba
203	Ložnice	5,37	Vinyl
204	Obývací pokoj	11,5	Vinyl
205	Kuchyň	4,1	Keramická dlažba

VÝPIS PŘEKLADŮ

OZN.	Typ Překladu	Délka uložení	Počet ks
P1	POROTHERM KP 7 2250mm	125mm	4
P2	POROTHERM KP 7 1750mm	125mm	4
P3	POROTHERM KP 7 1250mm	125mm	4
P4	POROTHERM KP 11,5 1500mm	125mm	2
P5	POROTHERM KP 11,5 1250mm	125mm	1
P6	POROTHERM KP 11,5 1200mm	120mm	1

LEGENDA MATERIÁLŮ

OBVODOVÉ ZDIVO
POROTHERM 30 PROFI

MEZIBYTOVÉ ZDIVO
POROTHERM RM30 AKU Z

NENOSNÉZDIVO
POROTHERM 11,5 AKU

TEPELNÁ IZOLACE
ISOVER GRAYWALL PLUS 200 mm

S

LEGENDA PRVKŮ

O OKNO

VP VNITŘNÍ PARAPET

D DVEŘE

P PŘEKLAD

VNP VNĚJŠÍ PARAPET

STUDENT	Petr Borecký	
VYUČUJÍCÍ	Ing. Jakub Mazura	
PŘEDMĚT	124 PSI1	FORMÁT: A3
		MĚŘÍTKO: 1:50
		DATUM: 28.11. 2024
OBSAH : Půdorys Typického Podlaží		Č. VÝKR.: 4a