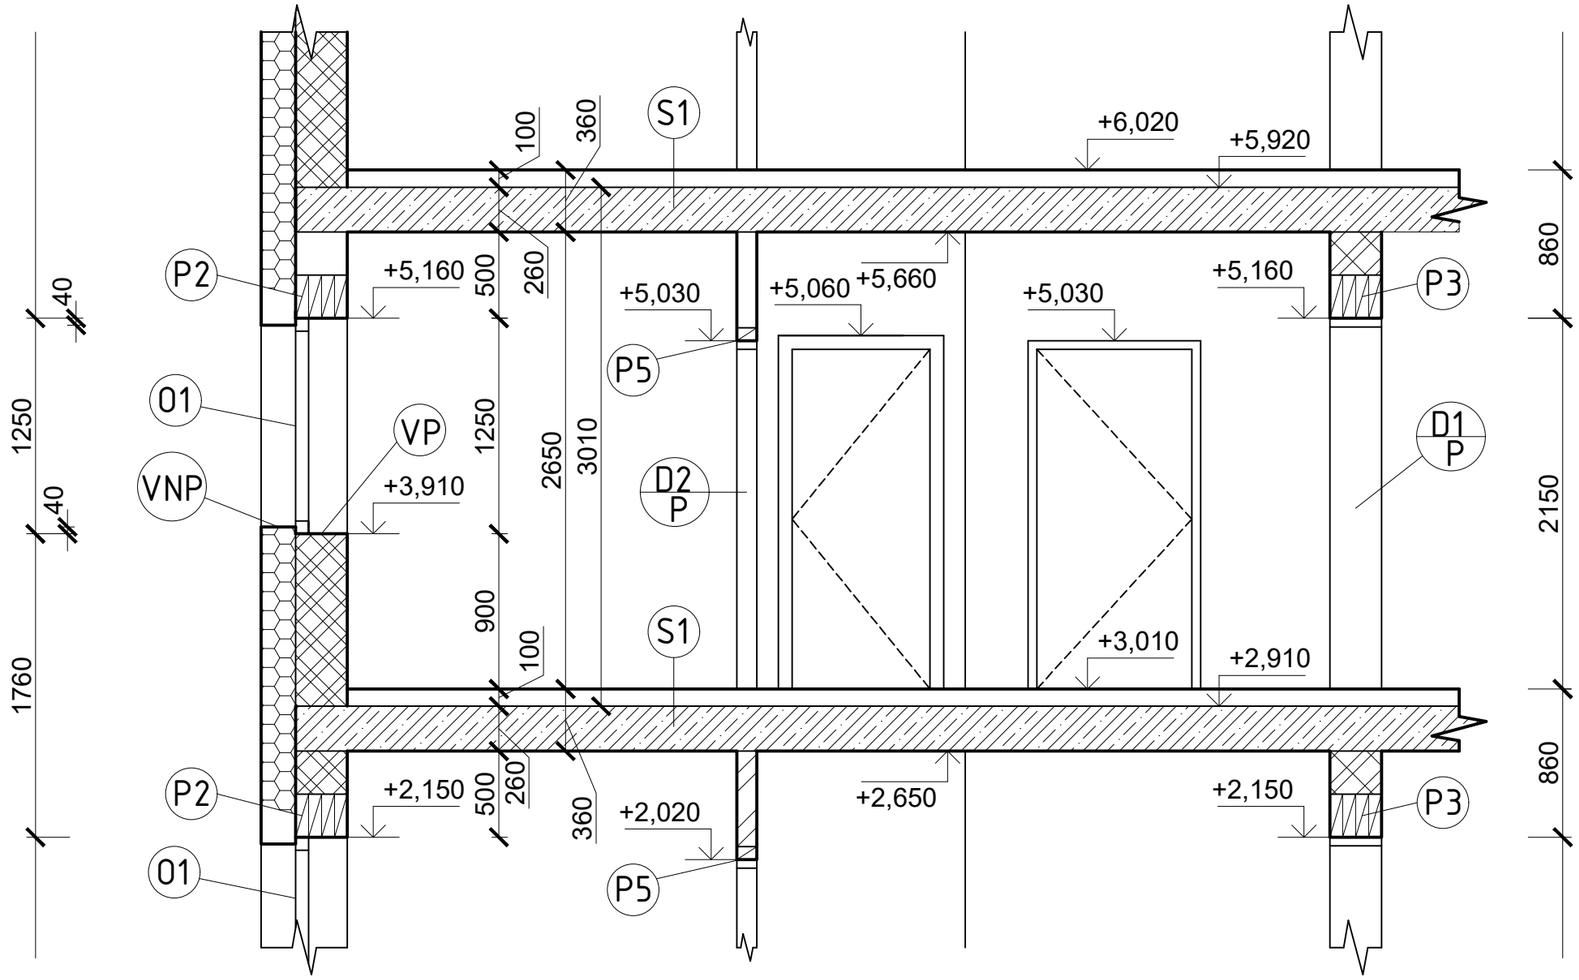

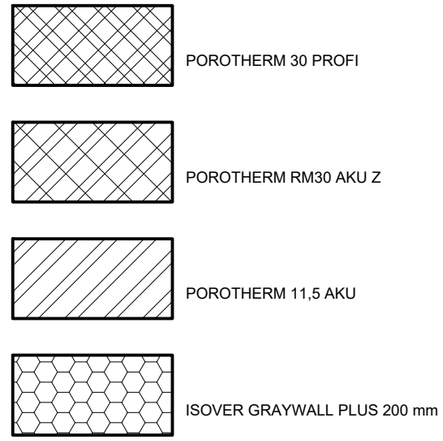

S1

- VINYL SYSTÉM CLICK 8 mm
- PODKLADOVÁ VRSTVA 2 mm
- BETONOVÁ MAZANINA 50 mm
- SEPARAČNÍ FÓLIE - mm
- KROČEJOVÁ IZOLACE (EPS) 40 mm
- ŽELEZOBETON 260 mm

O OKNO

VP VNITŘNÍ PARAPET

D DVEŘE

P PŘEKLAD

VNP VNĚJŠÍ PARAPET

S

STUDENT	Petr Borecký		
VYUČUJÍCÍ	Ing. Jakub Mazura		
PŘEDMĚT	124 PSI1	FORMÁT	A3
		MĚŘÍTKO	1:50
		DATUM	28.11. 2024
OBSAH : Řez Typickým Podlažím		Č. VÝKR.	4b