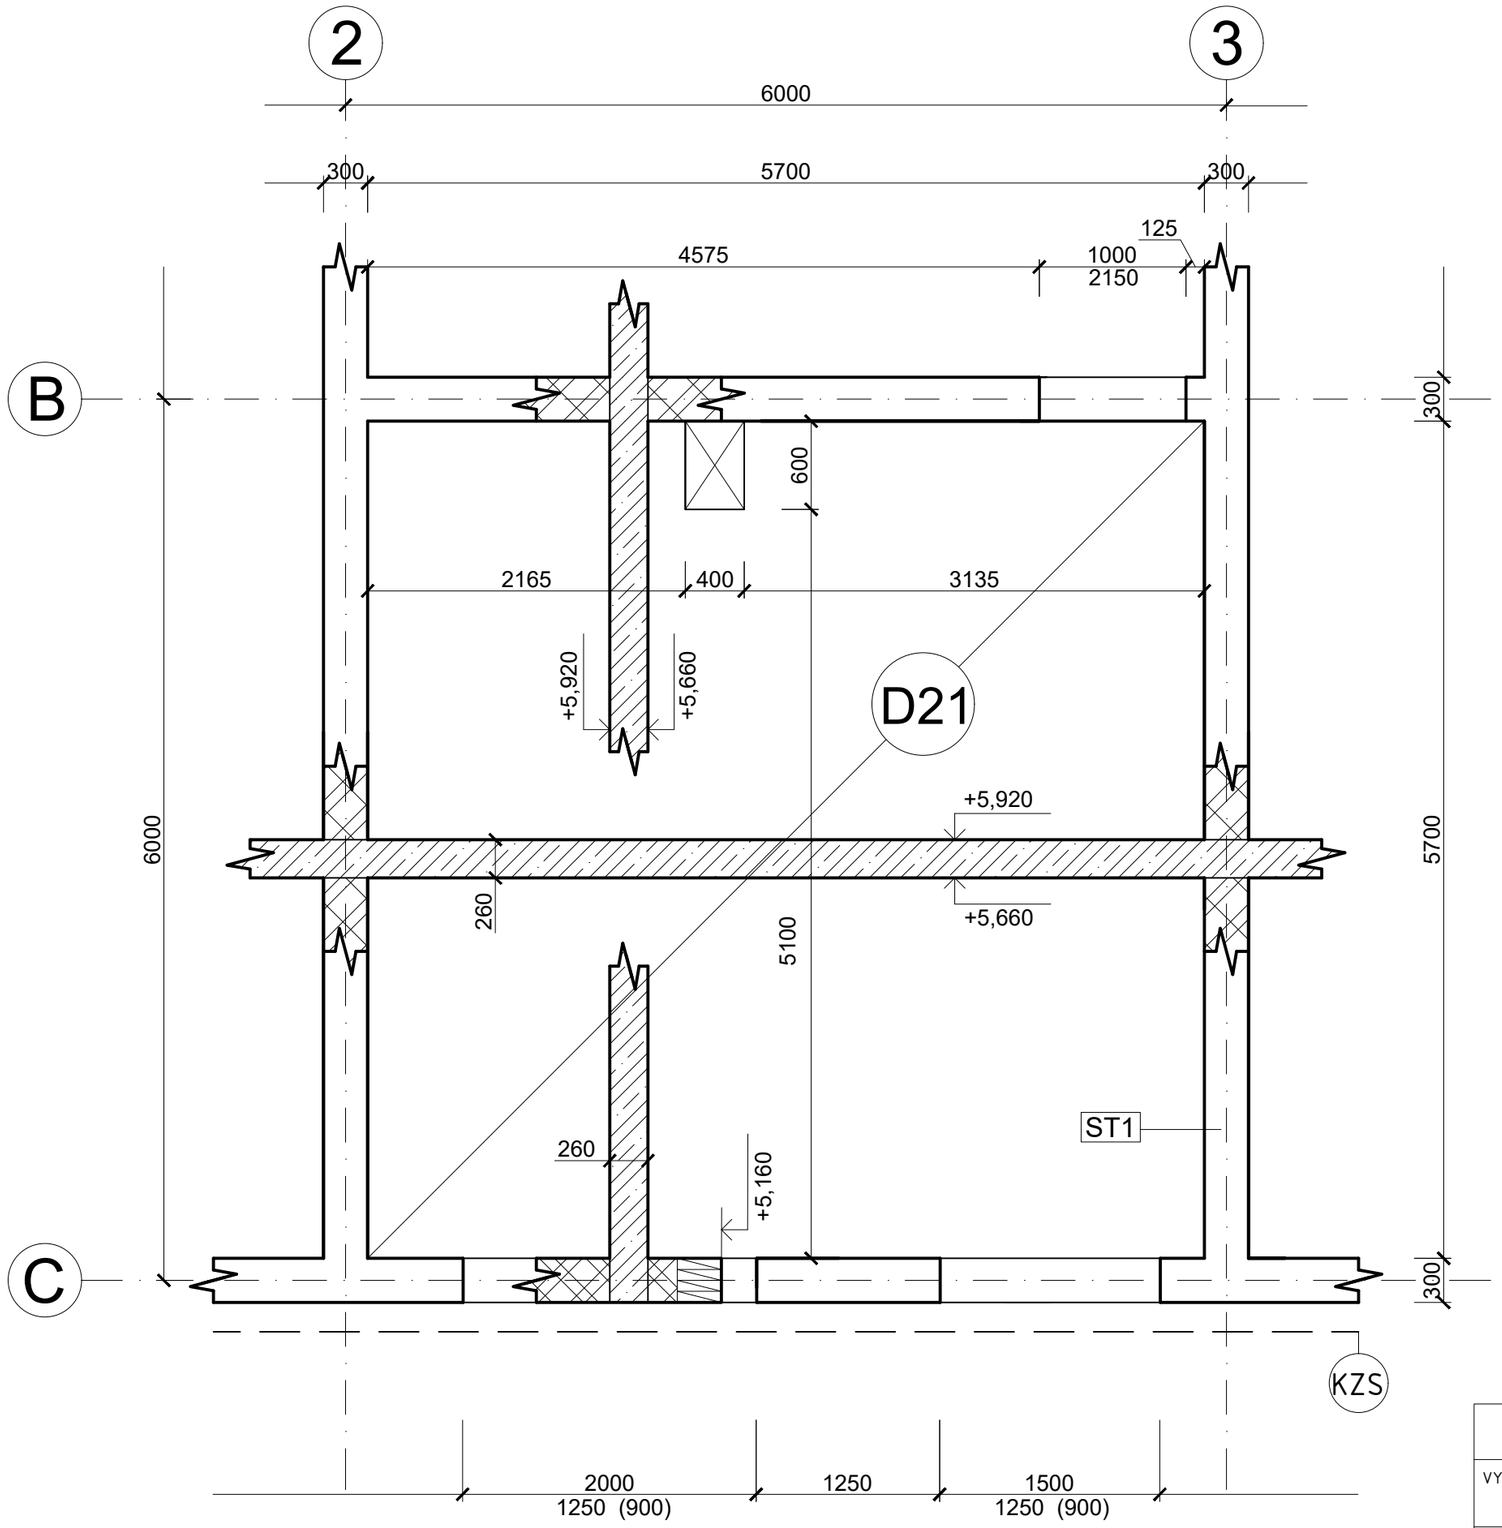

VÝPOČET

d = l/20 - l/25 = 6000/20 - 6000/25 = 300 - 240 mm
-> volím d = 260mm

LEGENDA MATERIÁLŮ

OBVODOVÉ ZDIVO
POROTHERM 30 PROFI

MEZIBYTOVÉ ZDIVO
POROTHERM RM30 AKU Z

NENOSNÉZDIVO
POROTHERM 11,5 AKU

S1 ŽB MONOLITICKÁ DESKA 260mm

ST1 ZDĚNÁ STĚNA 300mm

KZS KONTAKTNÍ ZATEPLOVACÍ SYSTÉM 200mm

S

Petr Borecký		
VYUČUJÍCÍ Ing. Jakub Mazura		
PŘEDMĚT 124 PSI1	FORMÁT	A3
	MĚŘÍTKO	1:50
	DATUM	1.12. 2024
OBSAH : Návrh monolitické stropní kce	Č. VÝKR.	5